




ПАНЕЛИ QUAD

Сборка

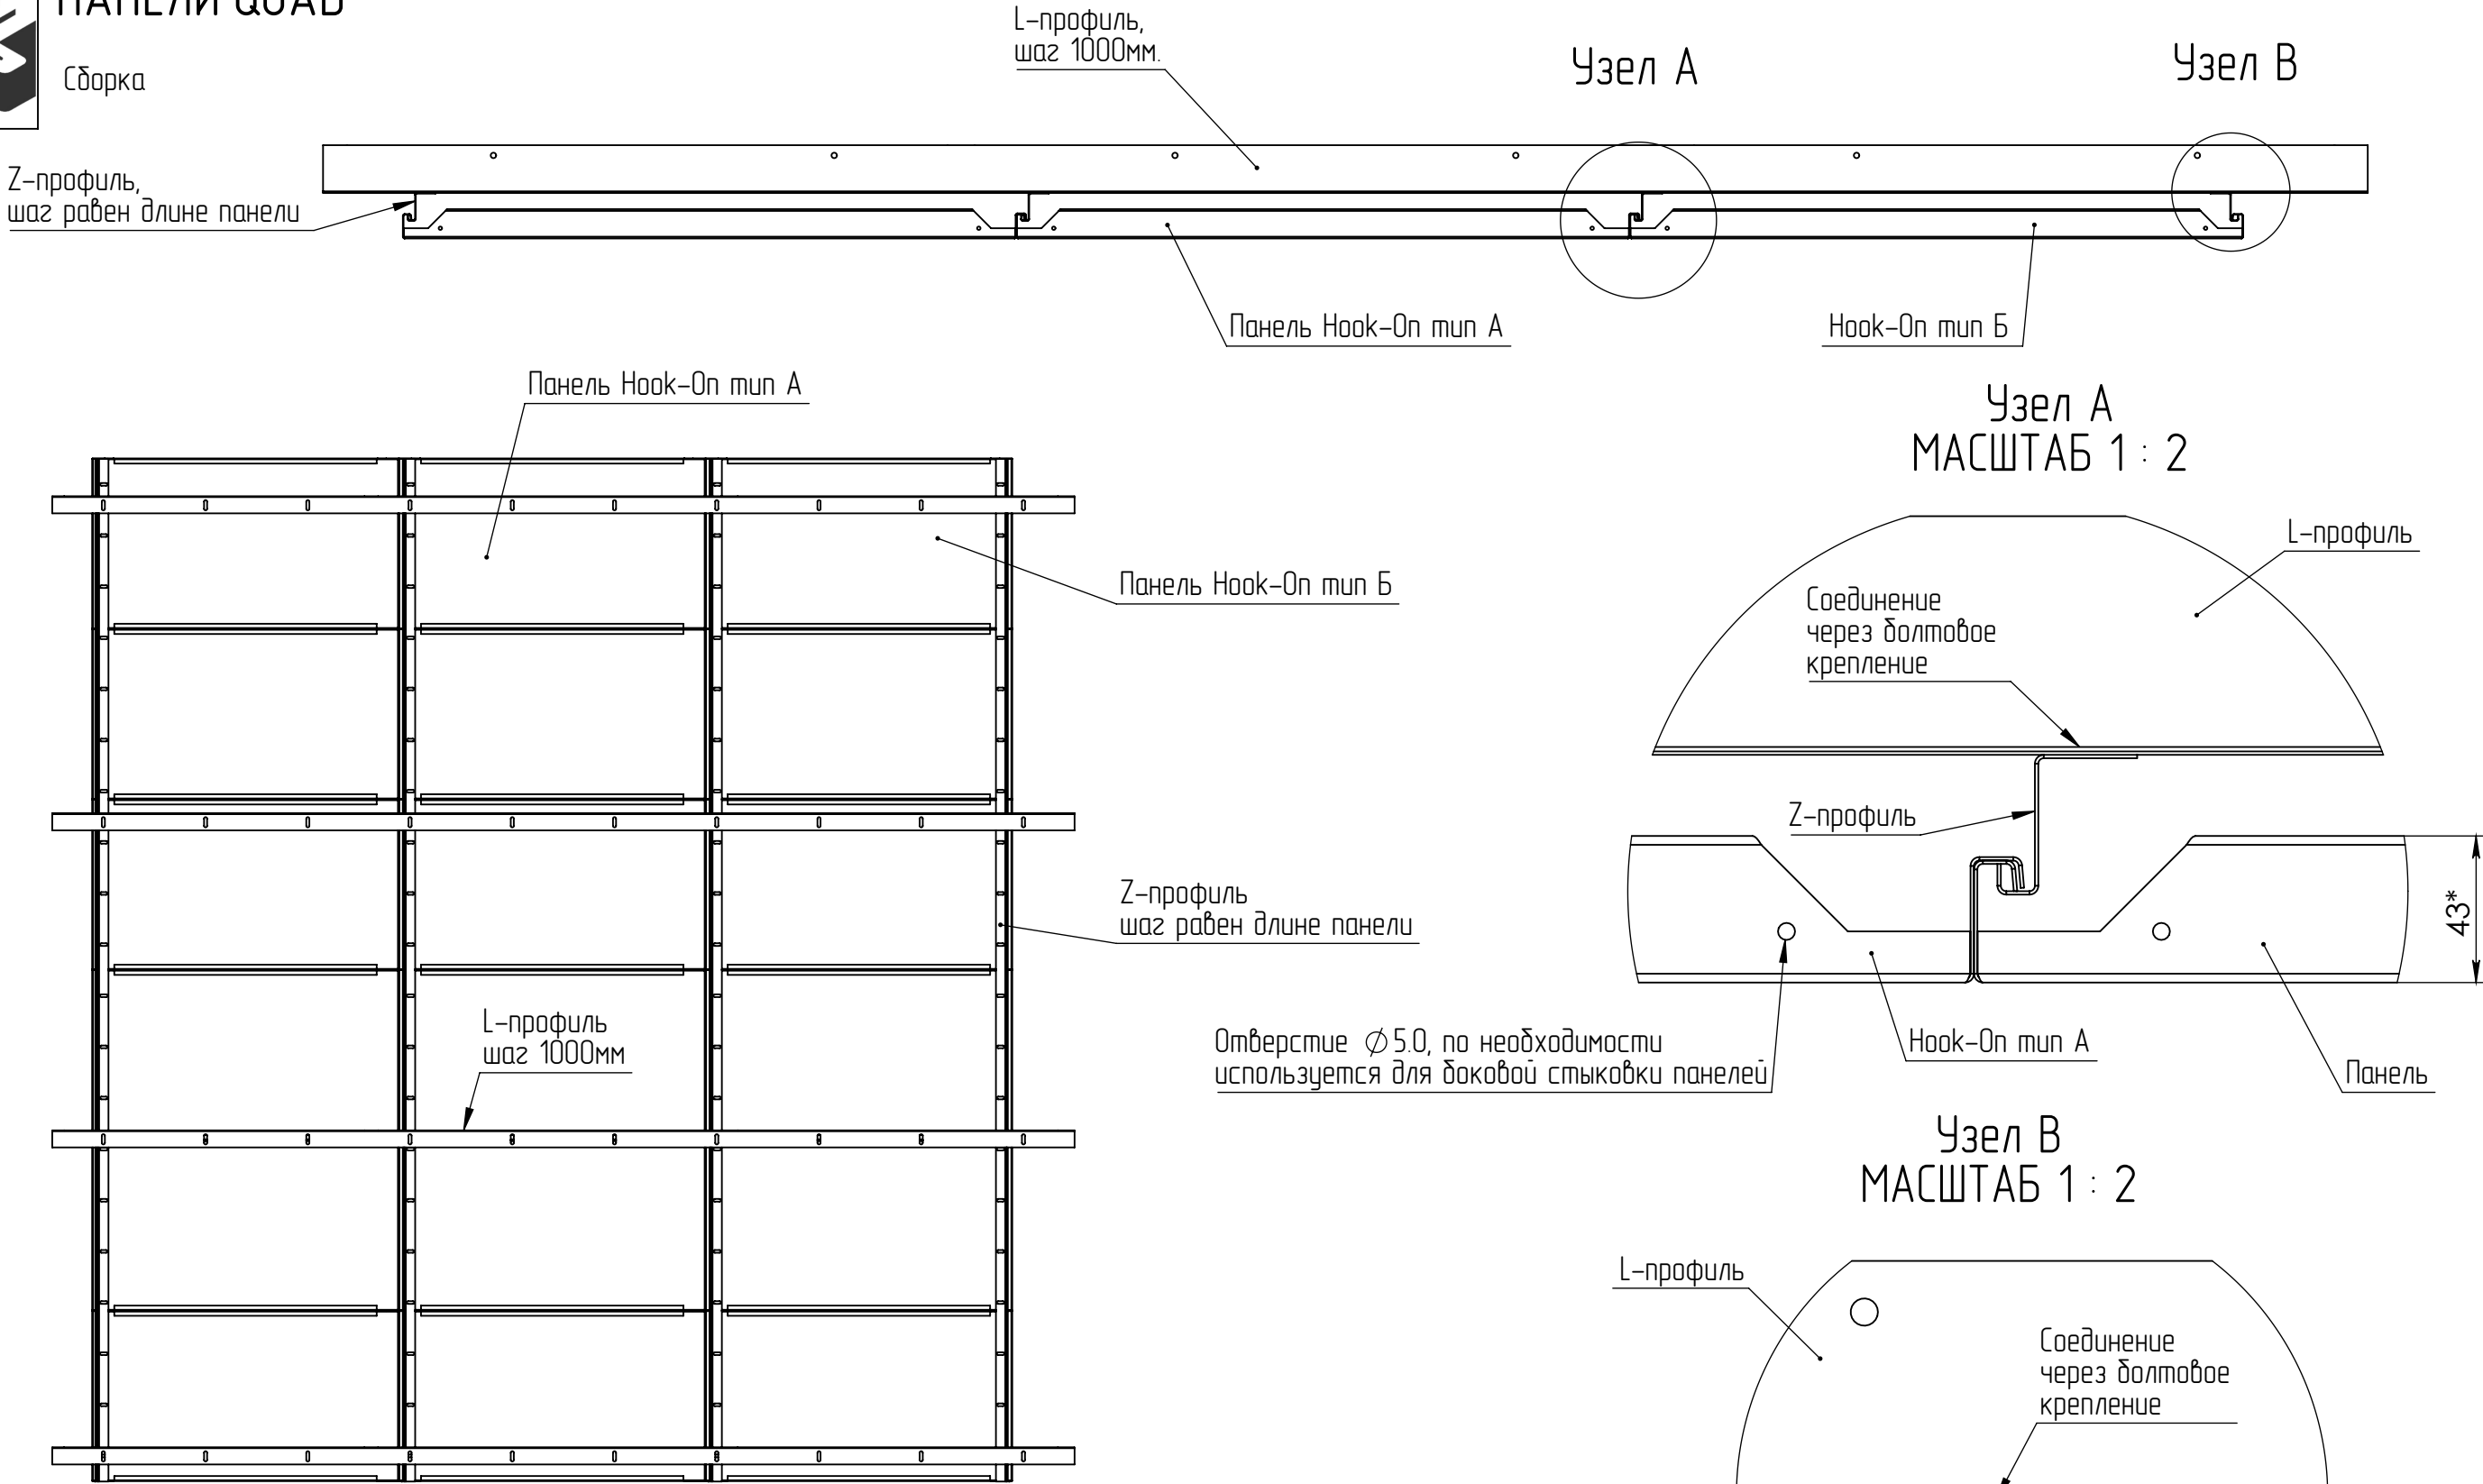

LWR

Примечание:
Панель типа Б является стартовой, с неё начинается монтаж перекрытия. Загибы с обеих сторон у этого типа панели выполнены вовнутрь, в отличие от типа А, что не создает зазор у стены и упрощает монтаж. Поскольку забариты монтируемой площади обычно не кратны длине/ширине- необходима подрезка панелей, мы предлагаем скрыть место реза предусмотренным профилем по периметру. Материал панелей "LWR PS" оцинкованная сталь, толщиной 0,7-1,0 мм. окрашивание порошковым методом в цвет RAL. Панели применяются для отделки потолка как внутри, так и снаружи помещений.

Разраб.		Подп.	Дата	Лист 5
Пров.				

LWR